NOT FOR CONSTRUCTION OR PERMIT UNLESS REVIEWED AND SEALED BY A LICENSED PROFESSIONAL ENGINEER OR ARCHITECT WHERE REQUIRED.

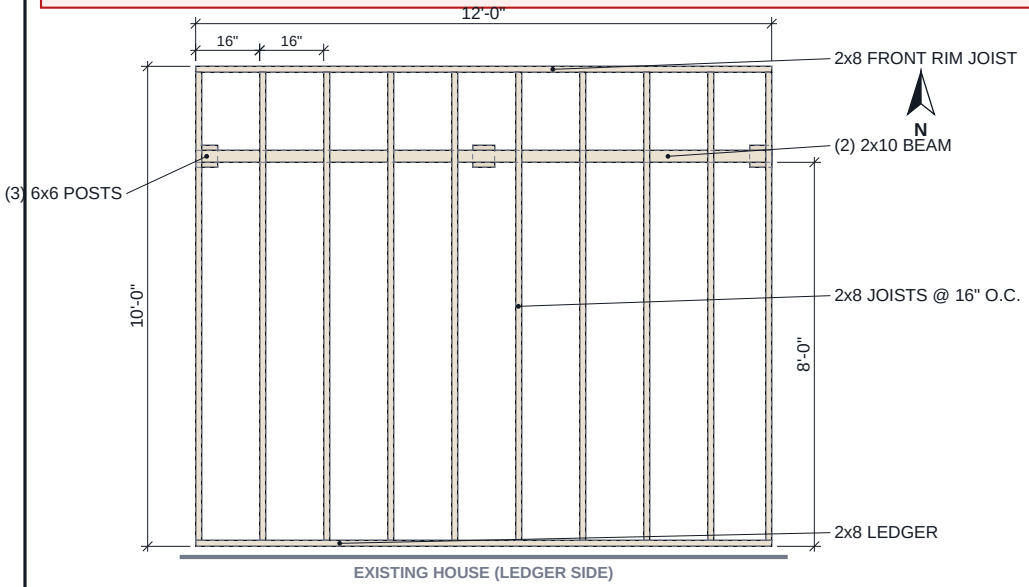

FRAMING PLAN

SCALE: 1/4"=1'-0" (DECKING NOT SHOWN, HIDDEN MEMBERS DASHED)

MEMBER SCHEDULE (PRELIMINARY)

1	(2) 2x10	12'-0"	Beam (2) 2x10
21	5/4x6	12'-0"	Deck board
1	2x8	12'-0"	Front rim joist
10	2x8	9'-9"	Joist
1	2x8	12'-0"	Ledger
3	6x6	1'-1/2"	Post 6x6

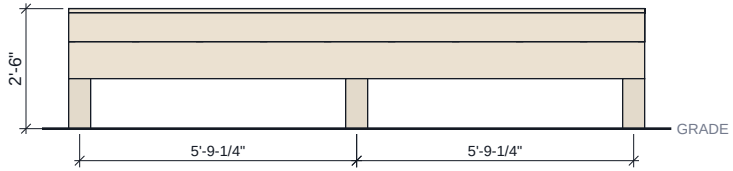

FRONT ELEVATION

SCALE: 1/4"=1'-0"

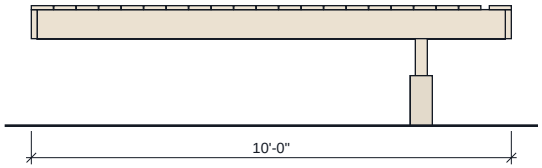

RIGHT ELEVATION

SCALE: 1/4"=1'-0"

REV	DATE	DESCRIPTION
A	10/23/26	Issued for review

0' 1' 2' 4'

GRAPHIC SCALE 1/4"=1'-0"

PRINT AT 100% / ACTUAL SIZE. DO NOT "FIT TO PAGE."

Dimensions in feet-inches; verify in the field before cutting.

Structural sizes are preliminary estimates, not engineering. Not code-reviewed.

Generated 10/23/2026 from Model Spec rev A.

1 in

CHECK SQUARE

Measure after printing:
it must be exactly 1 inch.

VIVID ENGINE SOLUTIONS

Vivid Build Studio drafting

PROJECT
12 x 10 Backyard Deck

CLIENT
Sample client

SHEET TITLE
Framing plan and elevations

DRAWN BY
Vivid Build Studio

DATE
10/23/2026

REVISION
A

SCALE
1/4"=1'-0"

SHEET
A-1